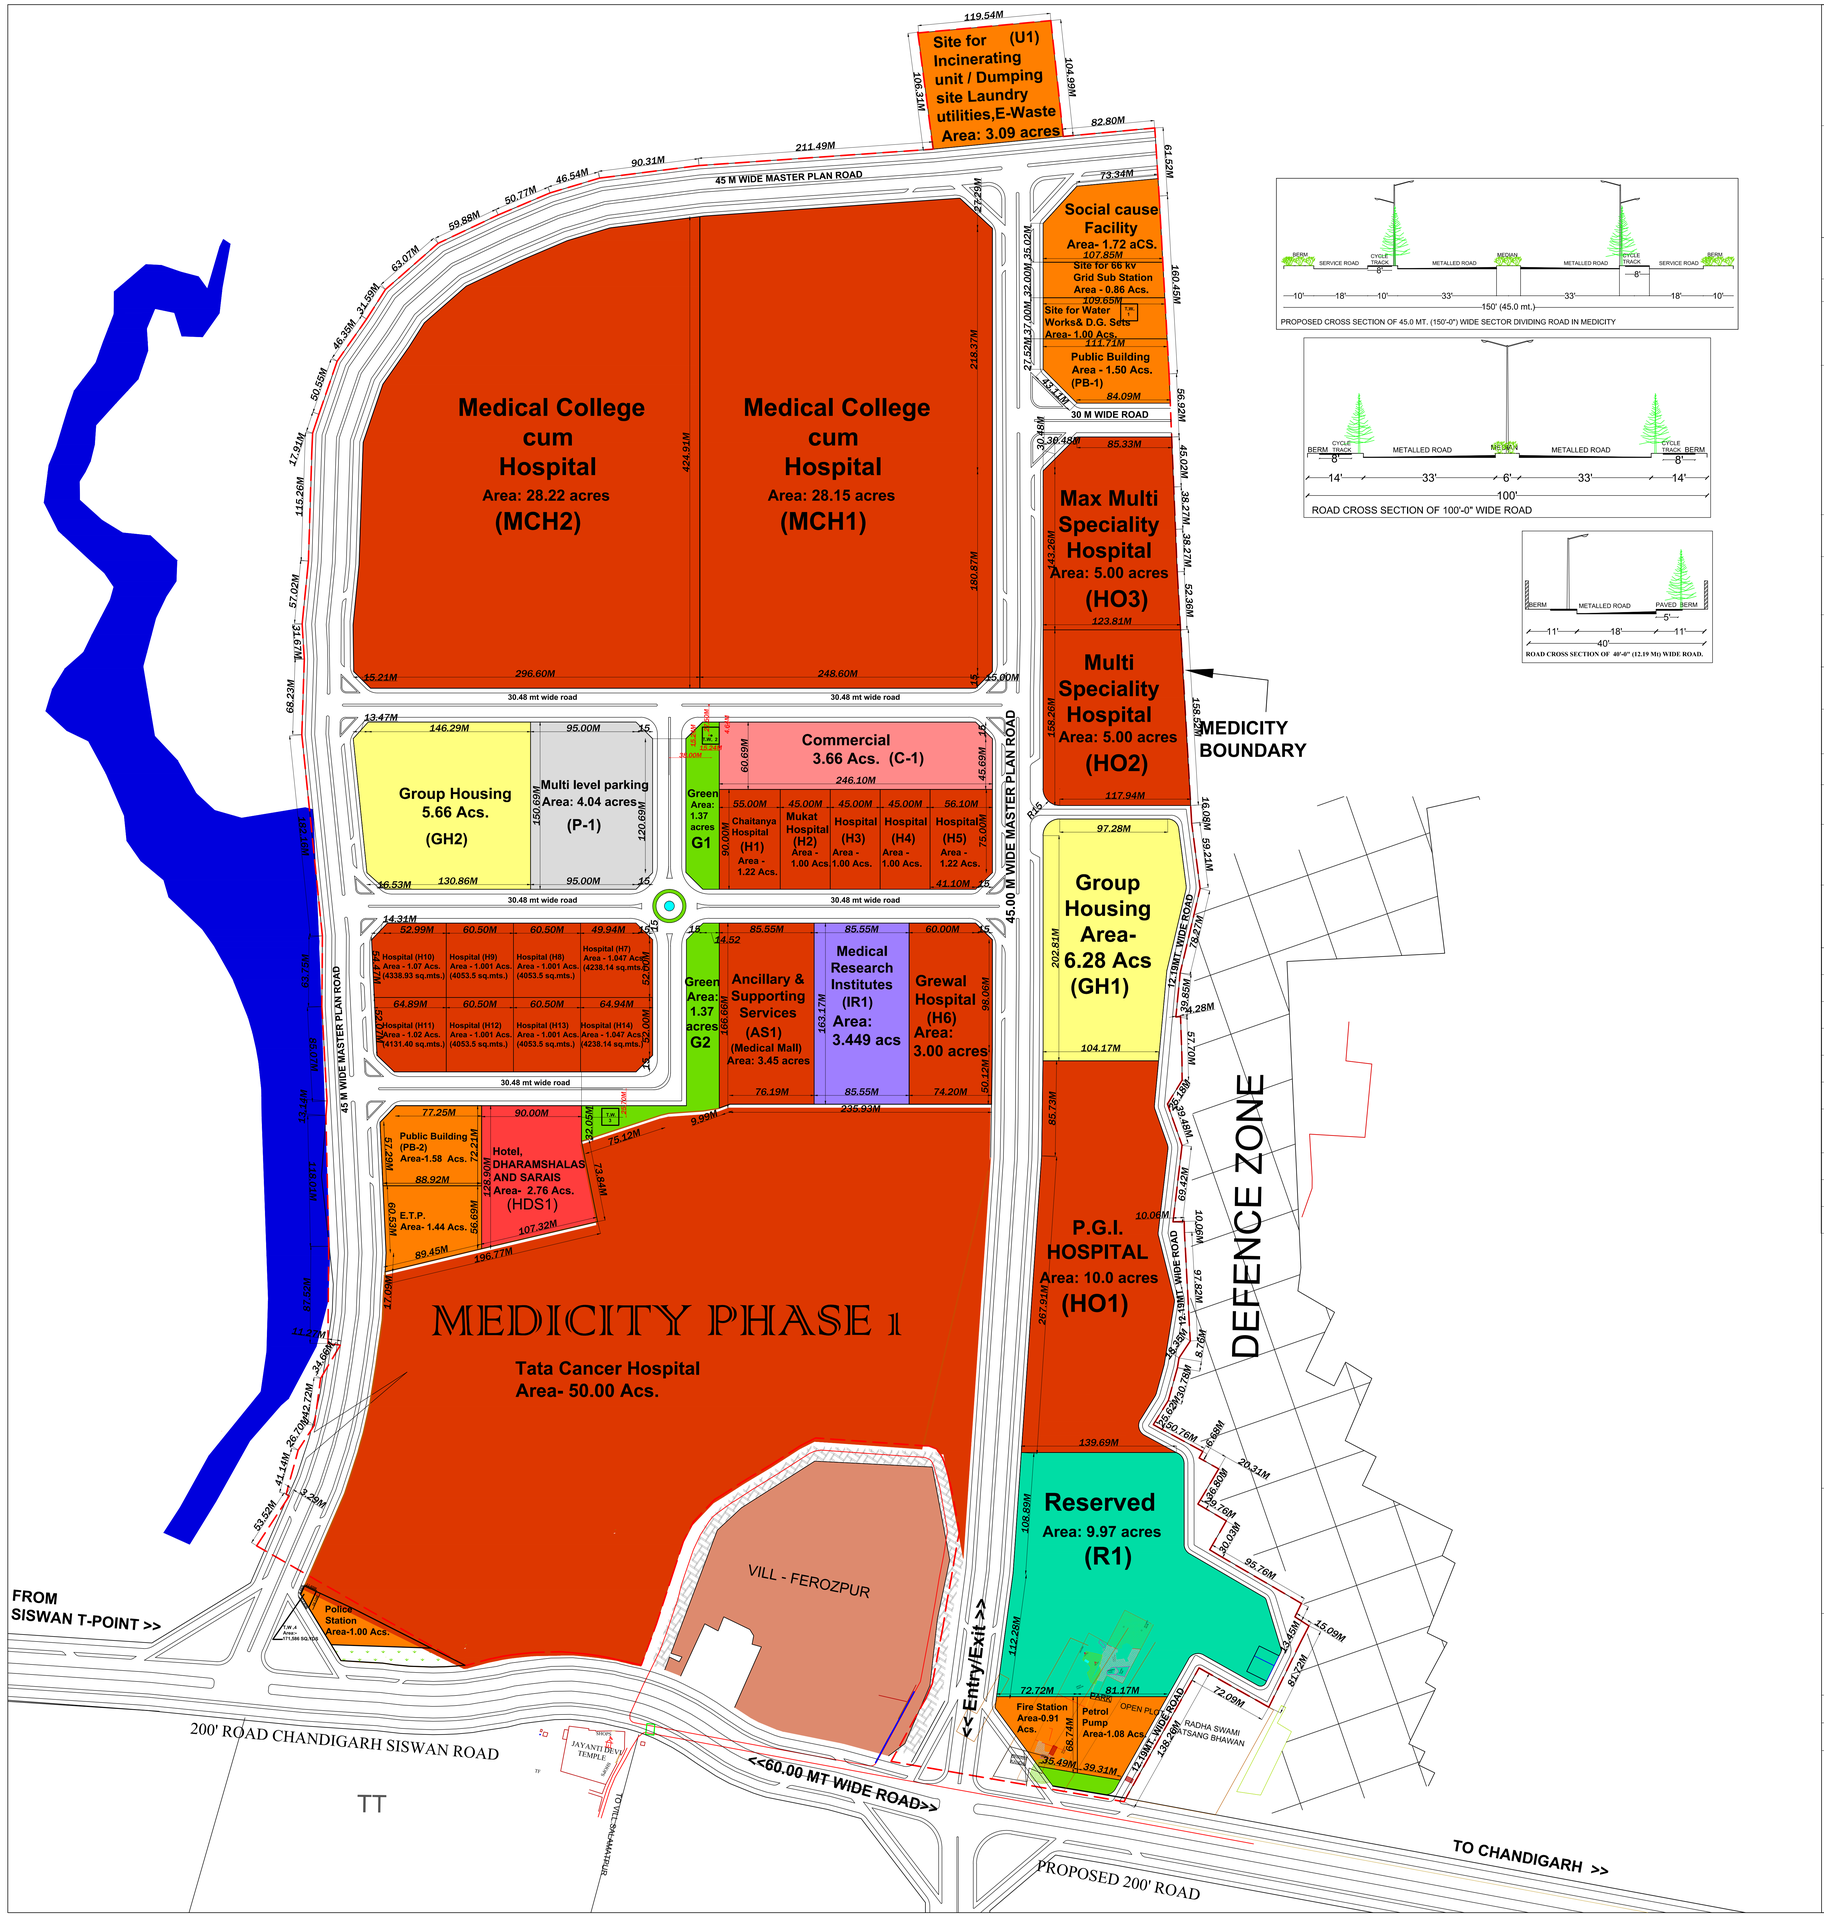

PROPOSED CROSS SECTION OF 45.0 MT. (150'-0") WIDE SECTOR DIVIDING ROAD IN MEDICITY

ROAD CROSS SECTION OF 100'-0" WIDE ROAD

ROAD CROSS SECTION OF 40'-0" (12.19 Mt) WIDE ROAD.

S.A.S.NAGAR

REALTY
For any Mohali Real Estate question, Whatsapp us 0091-7814833616

AREA DETAIL :-

AREA UNDER MEDICITY PHASE 1	= 97.425 ACS.
AREA UNDER MEDI CITY PHASE 2	= 161.25 ACS
TOTAL AREA UNDER MEDI CITY	**= 258.675 Acs.**

LAND USE			PLOT	AREA (IN ACS)
TATA CANCER HOSPITAL				50.00
MULTI SPECIALITY HOSPITAL			HO1	10.00
			HO2	5.00
			HO3	5.00
HOSPITAL	H1	1.22	H8	1.001
	H2	1.00	H9	1.001
	H3	1.00	H10	1.07
	H4	1.00	H11	1.02
	H5	1.22	H12	1.001
	H6	3.00	H13	1.001
	H7	1.047	H14	1.047
MEDICAL COLLEGE CUM HOSPITAL			MCH1	28.15
			MCH2	28.22
ANCILLARY & SUPPORTING SERVICES (Medical Mall)			AS1	3.45
GROUP HOUSING			GH1	6.28
			GH2	5.66
COMMERCIAL			C1	3.66
MEDICAL RESEARCH INSTITUTE			IR1	3.449
MULTI LEVEL PARKING			P1	4.04
Hotel, DHARAMSHALAS AND SARAIS			HDS1	2.76
INCINERATING UNIT / DUMPING SITE LAUNDRY UTILITIES,E-WASTE			U1	3.09
GREEN AREAS			G1	1.37
			G2	1.37
GRID SUB STATION				0.86
POLICE STATION				1.00
FIRE STATION				0.91
PETROL PUMP				1.08
PUBLIC BUILDING (PB-1)			PB-1	1.50
PUBLIC BUILDING (PB-2)			PB-2	1.58
WATER WORKS & D.G. SETS				1.00
SOCIAL CAUSE FACILITY				1.72
E.T.P.				1.44
RESERVED			R-1	9.97

Note:-
1. This drawing is based on Sketch No.D.T.P.(GMADA) 20/2015 Dated- 11/12/2015 which was approved in the Planning and Design committee's 12th meeting held on dated. 22.12.2015
2. This layout plan supercedes the all previous drawings.
3. Site for T.W. (site no.4) Area 171.586 sq.yds has been approved in the 57th R.P.D. meeting held on dated 13.03.2018 as agenda item no. 57.06.
4. Sites for T.W. (site no.1,2,3) size 50' x 50' has been approved in the 61st R.P.D. meeting held on 28.08.2018 as agenda item no. 60.03.

LAYOUT PLAN FOR MEDICITY, PHASE-1 & 2, NEW CHANDIGARH

OFFICE OF THE
DISTRICT TOWN PLANNER, SAS NAGAR.

Drawing No.D.T.P.(SAS Nagar) 2268/16 — Dated By:-26/05/2016

Drawn By:- Vinty — Checked By:- Sd/-

Sd/-	Sd/-	Sd/-	Sd/-
Asstt.Town planner	Distt.Town planner	Sr.Town planner	Chief.Town Planner (Punjab)