S.A.S. NAGAR

SECTOR - 53

(URBAN ESTATE PHASE III-A)

SCALE: 1" = 100'-0"

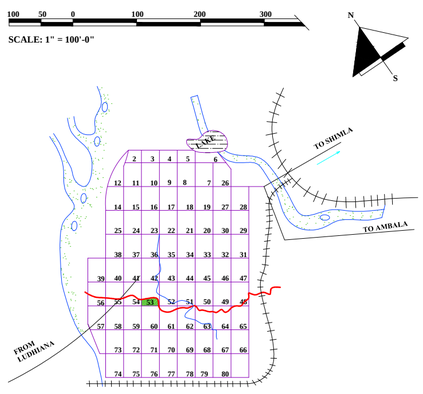

INSET PLAN

SCHEDULE OF AREAS:-

Acquired Area for SECTOR -53	101.08acs	
Area under Periphery Sector Road	10.12 acs	
Net Planned Area	90.96 acs	
1. Area under Plots	4.36 acs	(48.0%)
2. Area under Shopping Centre	3.03 acs	(33.0%)
3. Area under Educational Institutions	1.27 acs	(1.40%)
4. Area under Microwave Station	1.00 acs	(1.10%)
5. Area under Undetermind Use	3.93 acs	(42.0%)
6. Area under Reserved for Special Use	4.23 acs	(4.60%)
7. Area under For Tube well	0.12 acs	(0.10%)
8. Area under Roads & Open Spaces	34.02 acs	(37.4%)

SCHEDULE OF ACCOMMODATION:-

Category of Plot	Size of Plot	No. of Plots in Groups					Total No. of Plots	Plot Area (in sq. yds.)
		A	B	C	D	E		
7½ Marla	24'-9" x 70'-0"	-	-	236	-	-	236	192.50
10 Marla	33'-9" x 70'-0"	-	-	-	124	90	214	262.50
1 Kanal	50'-0" x 90'-0"	96	119	-	-	-	215	500.00
							665	

NOTES:-

1. All measurements are to be exact and checked at site.
2. All dimensions are to be taken from the centre line of carriage ways which are shown in dash & dots.
3. Radii of curves are given .
4. For junction treatment refer details.
5. For road sections referdrg.no. d.t.p (p) 394 / 69 & d.t.p., (p) 395/ 69
6. Site for primary school has been shifted as conveyed by C.T.P.S letter no. 1446 c.t.p /sc -17 dated 15-6-71.
7. Drawing corrected accordingly as per size specification on 17.3.72.
8. Site for primary school measuring 186'-9"x 176'-6" (area 0.76 acs) allotted to education deptt vide govt letter no. 3 /17 /90 /3 H.G-1 / 14826 dt.26.10.90.

REVISIONS:-

1. This drawing revised according to c.t.p.s instructions issued vide endst no.2464 c.t.p (pb) / sc-17 dated 1-8-75
2. This drawing supersedes drg. no. d.t.p (p) 439 / 70 issued by divisional town planner , patiala.
3. One kanal block containing plots from 44-54 shifted by 14 ft. towards the undermined use area.
4. 7½" marla block containing plot nos . 200 - 219 shifted by 2 feet towards 60'-0" wide road.
5. 10 marla block containing plot nos 452 -484 shifted by 3 feet towards 100'-0" wide sector road.
6. One kanal block containing plot nos 579-602 shifted by 5 feet towards 60'-0" wide road.
7. Site of additional tube well incorporated wide this office memo no. d.t.p (mohali) ms - 53 dated 19.12.75
- Site for rest house has been approved vide c.t.p letter no 1574 c.t.p (pb) / sc-73 dated 17.7.92 (area :=0.37 acs)
- Site of yatri niwas approved in the design and layout plan approval committee meeting held on 19.4.95

ADDITION & ALTERATIONS"-

1. The block of one kanal plots no 44-to 54 shifted towards road by 14'-0" & brought to its original position as per drg. d.t.p (p) 439 /70 dated 12.8.1975.
2. The acquisition boundary corrected as per actual demarcation at site given by the l.a.o punjab.
3. New plot no. 655 to 665 added on 26.5.1980 as per decision conveyed by the pb.govt vide letter no. 3 / 26 / 80 -2 ud (i) dated 26.5.80
4. Govt /private schools identified as approved by c.t.p (pb) wide his letter no. 1514 c.t.p (pb) dated 23.5.89
- This drawing has been traced from drg.no. 75/11 dated 28.5.75 , incorporating schedule of areas.
- The construction of basement has been permitted in the residential plots up to 399 sq.yds should confirm to the conditions laid down in the letter no. phb -dtp 92 / 1214 dated 6.2.92 issued vide chief administrator , urban estate ,punjab proposed site for centenary bhawan area 2.251 acrs marked as per divisinal town planner pb. housing devp. bard end no. 93/ss-8/1/65 dated 6.12.93
- Plot has 655 to 665 restored as govt. approval conveyed by add. housing commissioner vide memo no. 1943-44 dated :2.2.2004 and plan approved vide chief town planner no. 1846 C.T.P (PB) SC-76 dated 27-6-94 .
- The site for private nursery school has been converted into primary school as per puda letter no.4788 dated 25.5.99
- Plot no. 655 measuring (50'x90') have been omitted new 10 marla plots measuring (35'xas par site have been provided as decided by c.a puda in the meeting held on 7.3.2000
- The revised layout plan as above has been approved by s.t.p vide his letter no.550-s.t.p (s)-55-12 dated 28.3.2000
- Dimension in plots no 655-671 have been added as per s.t.p. PUDA'S memo no; PUDA-tpw - 00/ 3771 dt 4-7-2k
- Site for Bhachat Bhawan has been converted in to cultural complex as per decision in the regional planning & design committee meeting held on 29-11.2000 .

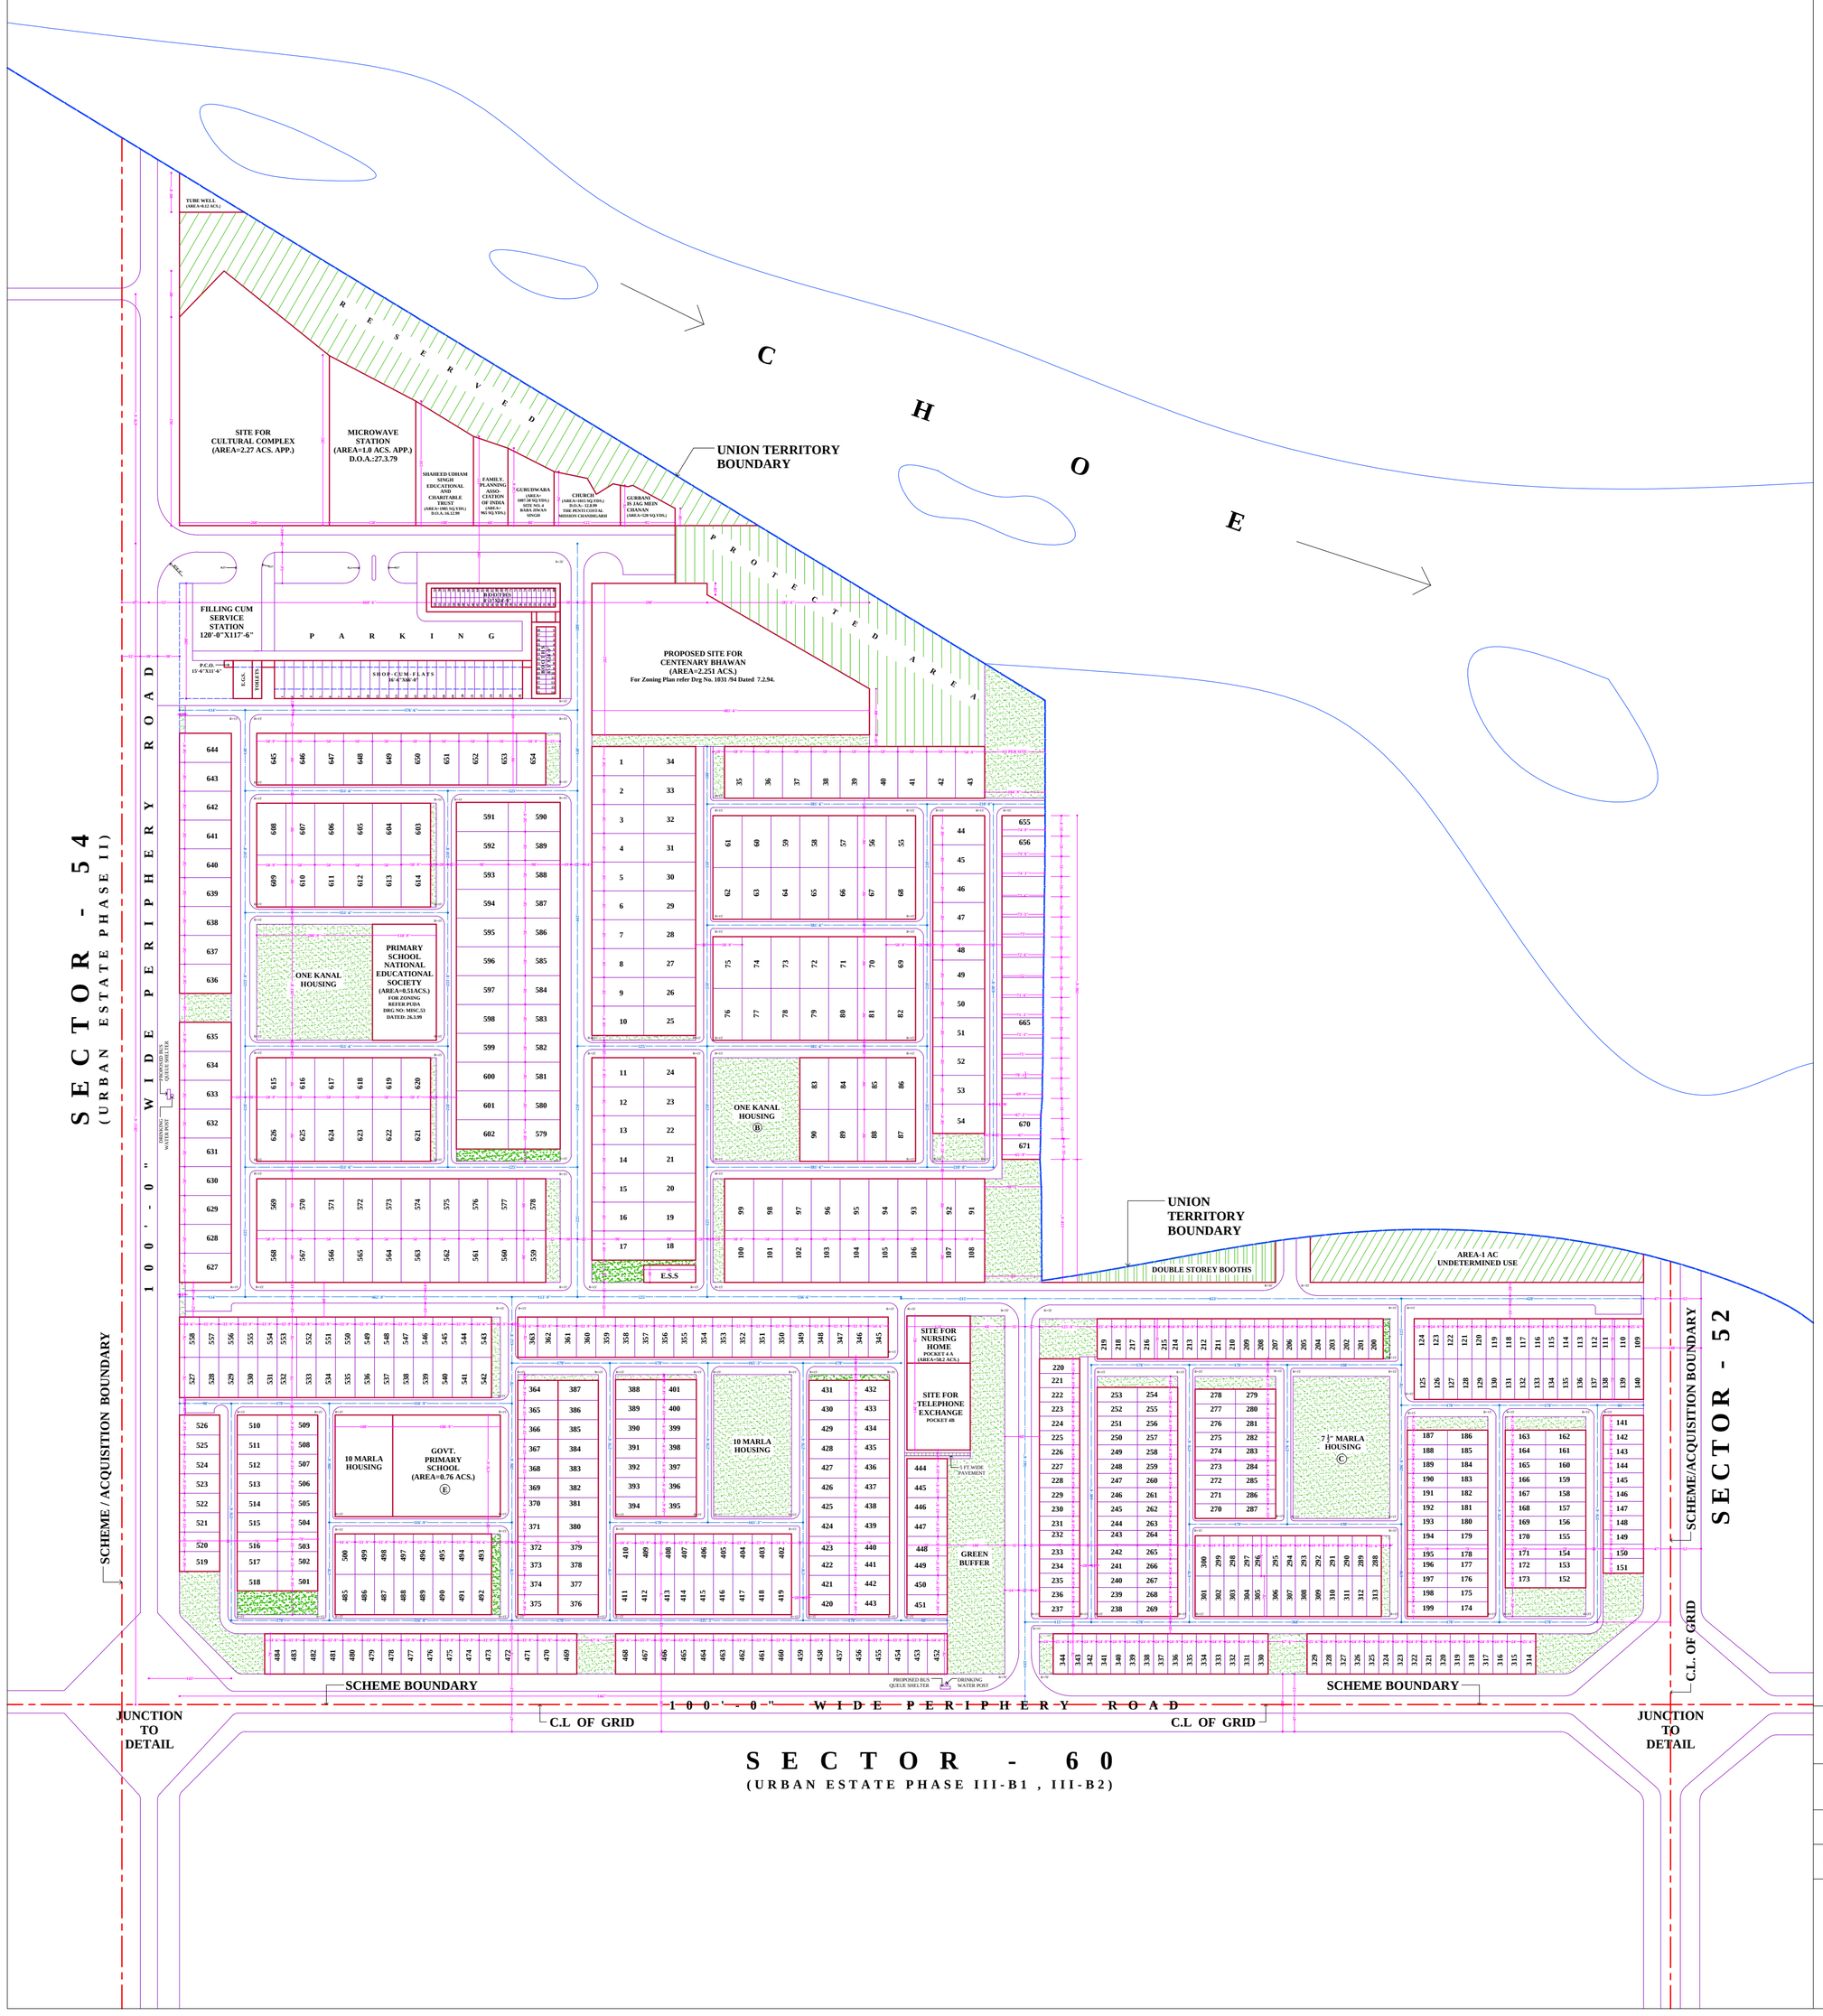

NOTE:-

THIS DIGITIZED DRAWING IS BASED ON THE ORIGINAL DRAWING OF THE CONCERNED DEPARTMENT. IN CASE OF ANY DISCREPANCY THE DETAILS IN THE ORIGINAL DRAWING SHALL PREVAIL UPON.

DEMARCATION PLAN & NUMBERING PLAN, SECTOR - 53

OFFICE OF THE DIVISIONAL TOWN PLANNER S.A.S NAGAR

DRG. NO: DTP (SAS NAGAR) 669/89 DATED: 28.8.89

TRACED BY: CHECKED BY:

- Sd -	- Sd -	- Sd -	- Sd -
Planning Asstt.	Asstt. Town Planner	Divl. Town Planner	Chief Town Planner

REALTY HOLDING & MANAGEMENT CONSULTANTS
For any Mohali Real Estate question,
whatsapp us @91-7814613916
realtyconsultants.in