S.A.S. NAGAR

SECTOR - 60

(URBAN ESTATE PHASE III-B1 & III-B2)

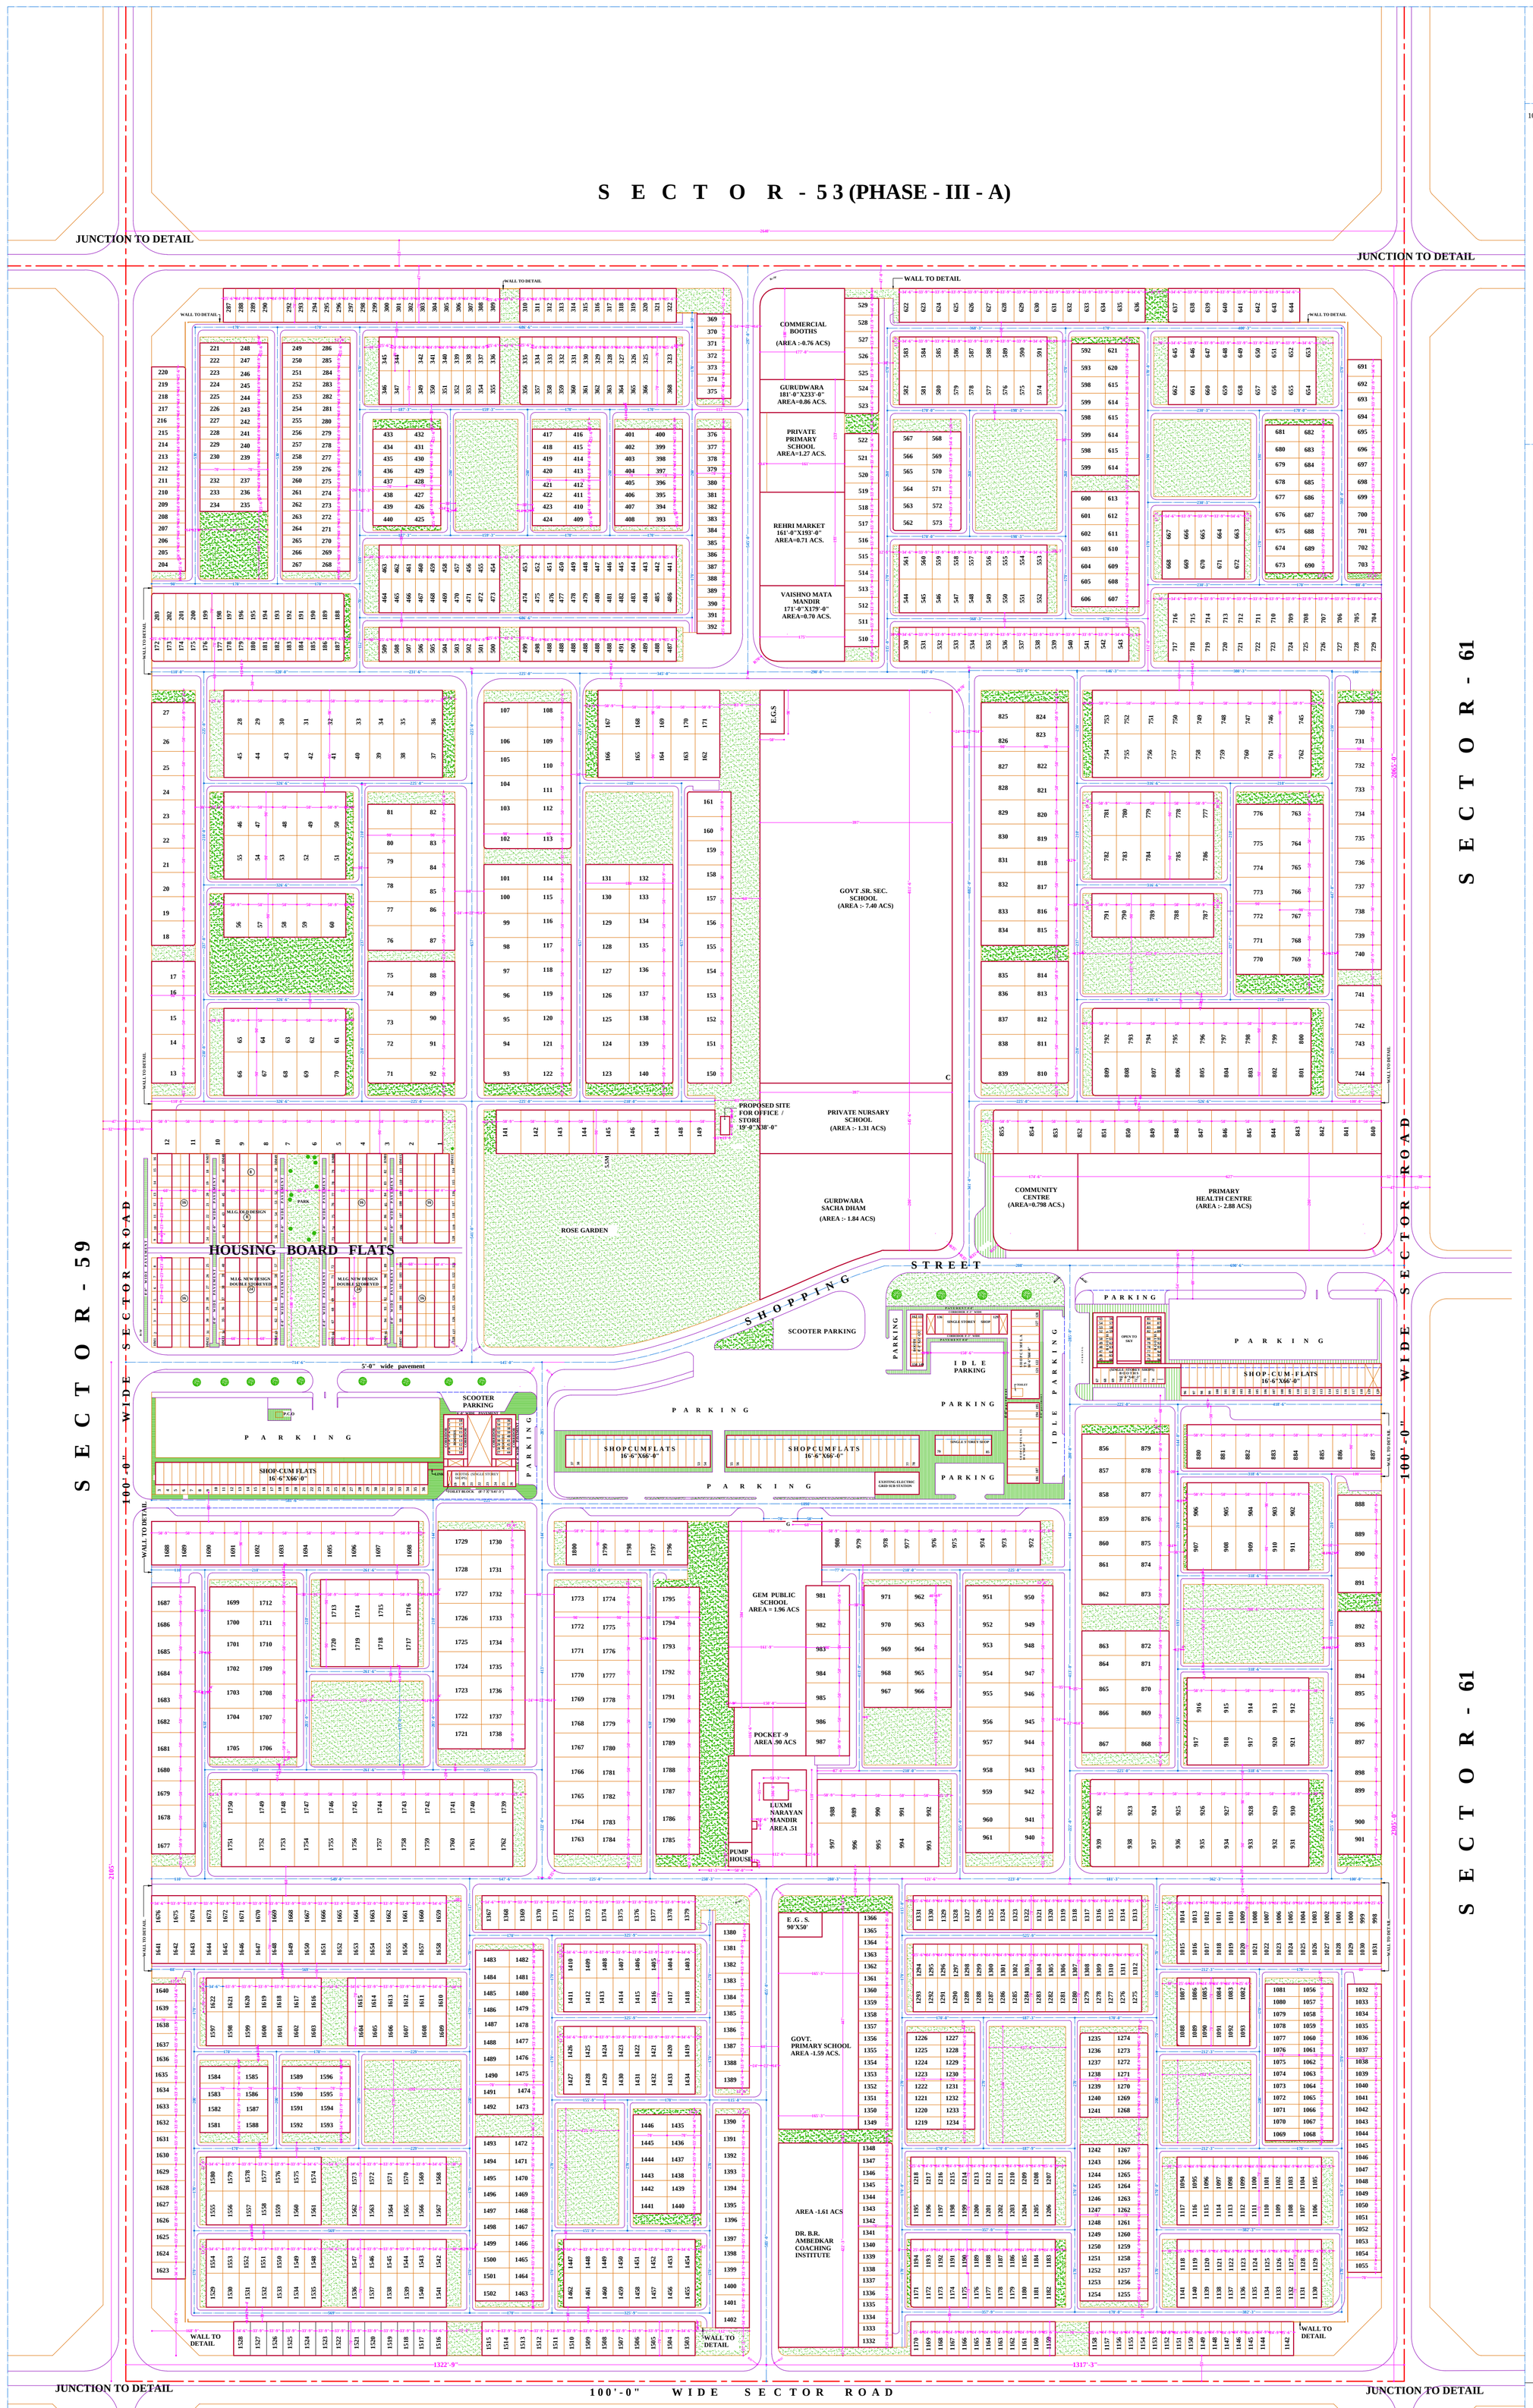

SCALE : 100 FEET TO AN INCH .

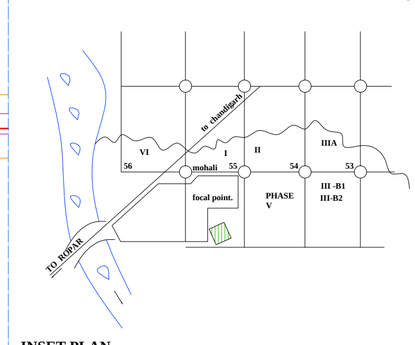

INSET PLAN

Category	size of plots. plots.	area sq.yds.	no of plots in groups. A	B	C	D	E	F	G	H	total. PLOTS
7 ½"marla	24'-9"X70'-0"	192.5	-	338	-	-	-	369	-	-	707
10 marla	33'-9"X70'-0"	262.5	-	-	220	-	-	-	310	-	530
One kanal	50'-0"X90'-0"	500.0	-	-	-	126	142	-	-	124	563
										TOTAL PLOTS:	1800.

SCHEDULE OF AREAS:-

1.	Area under plots	115.24 Acs.	45.35%
2.	Area under govt housing	5.79 Acs.	2.25%
3.	Area under shopping centre	12.00 Acs.	4.70%
4.	Area under special use	1.43 Acs.	0.55%
5.	Area under public buildings	19.30 Acs.	7.55%
6.	Area under reserve use	4.90 Acs.	1.90%
7.	Area under roads	56.39 Acs.	2230%
8.	Area under open spaces.	39.18 Acs.	1540%
	Total	254.77 Acs.	100%
	Area under peripherial roads	15.10 Acs.	
	Grand Total	269.87 Acs.	

NOTES:-

1. All measurements are to be exact should be checked at site.
2. All dimensions are to be taken from the centre line of carreage ways which are in dash & dots.
3. Position of existing trees are shown but laying out in no case should be done by taking mearurements from from them.
4. Detail of shopping centre will be supplied latter on.
5. For juction treatment refer details .
6. Details road cross section will be supplied latter on.
7. Radii of curve are shown.
8. This drawings is redrawn from drawing no d.t.p (mohali) 15 /17 dated 26.10.71

- Govt. / private schools identified as approved by c.t.p.(pb) vide letter no. 15 14 c.t.p (pb) / sp -275 dated 23.5.89.
- Site for primary school measuring 165'-3" x 447''-0" -50' x 90' = (area 1.59) allotted to education deptt. vide govt letter no.31 / 17 / 90 /9 /3 h.g.i /14826 dated 26-10-90
- Parking in front of 96 to 100 and boths from 86 to 89 has been ammended vide c.t.p's letter no.1204 c.t.p (pb) sc-57 dated 1-6-92.
- The size of plot no. 681-c & 682-c have been increased from 34'-6"x 70'-0" to 40'-0" x 70 -0" as per chief administrator puda letter a-3-puda (f-8) 96 / 4267 dated 22.1.96
- Entry point to pocket 'a' parking infront of s.c.f 3 to 36 has been amended vide s.t.p. ,s.a.s nagar memo ,no. 393 s.t.p (s) ss.13 dt. 5-3-98
- The pvt. nursery school site (1.56 acs) and pocket -9 (0.40 acs) south of site has been converted into high school site as per stp puda s letter no. 2586 dated 12.3.99.
- Site reserved earlier for cinema site is now he used for commercial shopping game and mini theatre as per decision taken in the planning and design committee meeting held on 29.7.98
- Size of the site (earlier cinema) has been reduced to 193'-6" x 128'-3" vide c.t.p's memo no. 1618-19,sc-57 dated 23-6-99.

NOTE:-

THIS DIGITIZED DRAWING IS BASED ON THE ORIGINAL DRAWING OF THE CONCERNED DEPARTMENT. IN CASE OF ANY DISCREPANCY THE DETAILS IN THE ORIGINAL DRAWING SHALL PREVAIL UPON.

LAYOUT CUM DEMARCATION PLAN, SECTOR - 60

OFFICE OF THE DIVISIONAL TOWN PLANNER S.A.S NAGAR

DRG. NO: (D.T.P S.A.S. nagar) 612/88 DATED: 18.2.88

TRACED BY: CHECKED BY:

- Sd -	- Sd -	- Sd -	- Sd -
Planning Asstt.	Sr. Asstt. Town Planner	Divl. Town Planner	Chief Town Planner

REALTY HOLDING & MANAGEMENT CONSULTANTS
For any Mohali Real Estate question,
whatsapp us @91-7814613916
realtyconsultants.in