S.A.S. NAGAR
SECTOR - 67

SCALE: 1" = 100'-0"

INSET PLAN

DETAIL OF AREAS	IN ACS.
Area under pocket no. 1	15.726 Acs.
Area under pocket no. 2	17.522 Acs.
Area under pocket no. 3	8.838 Acs.
Area under Air Force / Naval housing	9.700 Acs.
Area under Danga Pirat Housing	4.200 Acs.
Area under Institutional	5.358 Acs.
Area under Water Works	1.950 Acs.
Reserved Area	3.234 Acs.
	28.930 Acs.
Area under Commercial / Corporate offices	31.005 Acs.
Area under Roads & Leisure valley	
	126.463 Acs.
Total area of scheme	

ROAD CROSS SECTION

200'-0" WIDE ROAD

100'-0" WIDE ROAD

80'-0" WIDE ROAD

60'-0" WIDE ROAD

40'-0" WIDE ROAD

36'-0" WIDE ROAD

30'-0" WIDE ROAD

28'-9" WIDE ROAD

28'-6" WIDE ROAD

30'-0" WIDE SERVICE LANE

NOTES:-

- Site for Temple (Mandir) has been allotted vide GMADA'S Endst No. GMADA / E.O. / 2011 / 14923 Dated 16.11.2011.
- Site for Gurudwara Sahib has been allotted vide GAMADA'S Endst No. GMADA / E.O / 2011 / 13924 Dated 4.11.11.

NOTES:-

1. Three Tube well sites measuring 25'X25' has been marked as per divisional Engg.(PH 2 P.H.D.B approval dt. 26.5.96.
2. This drawing is based on Drg. No. 01 job no. m-67 dated 19-1-2000 supplied by P.U.D.A.
3. Site for Noval Group Housing area has been rated in layout plan as per PUDA Drg. No. 01 . 108 sent vide Endst No. PUDA'S
4. Site for Danga Pirat Society area 4.20 Acs. has been incorporated in layout plan as per PUDA'S Drg. No. 01 Misc-67 sent vide ends no. PUDA'S
5. This drawing has been amended as per PUDA 03 Job No. M-67 dated 30-5-2001 sent vide No. PUDA'S T.P.V - 01 / 80 dated 14.6.01
6. Site of vocational institute has been marked as per information received by puda letter no. TPW 04 / 47 / dated 3.2.89.

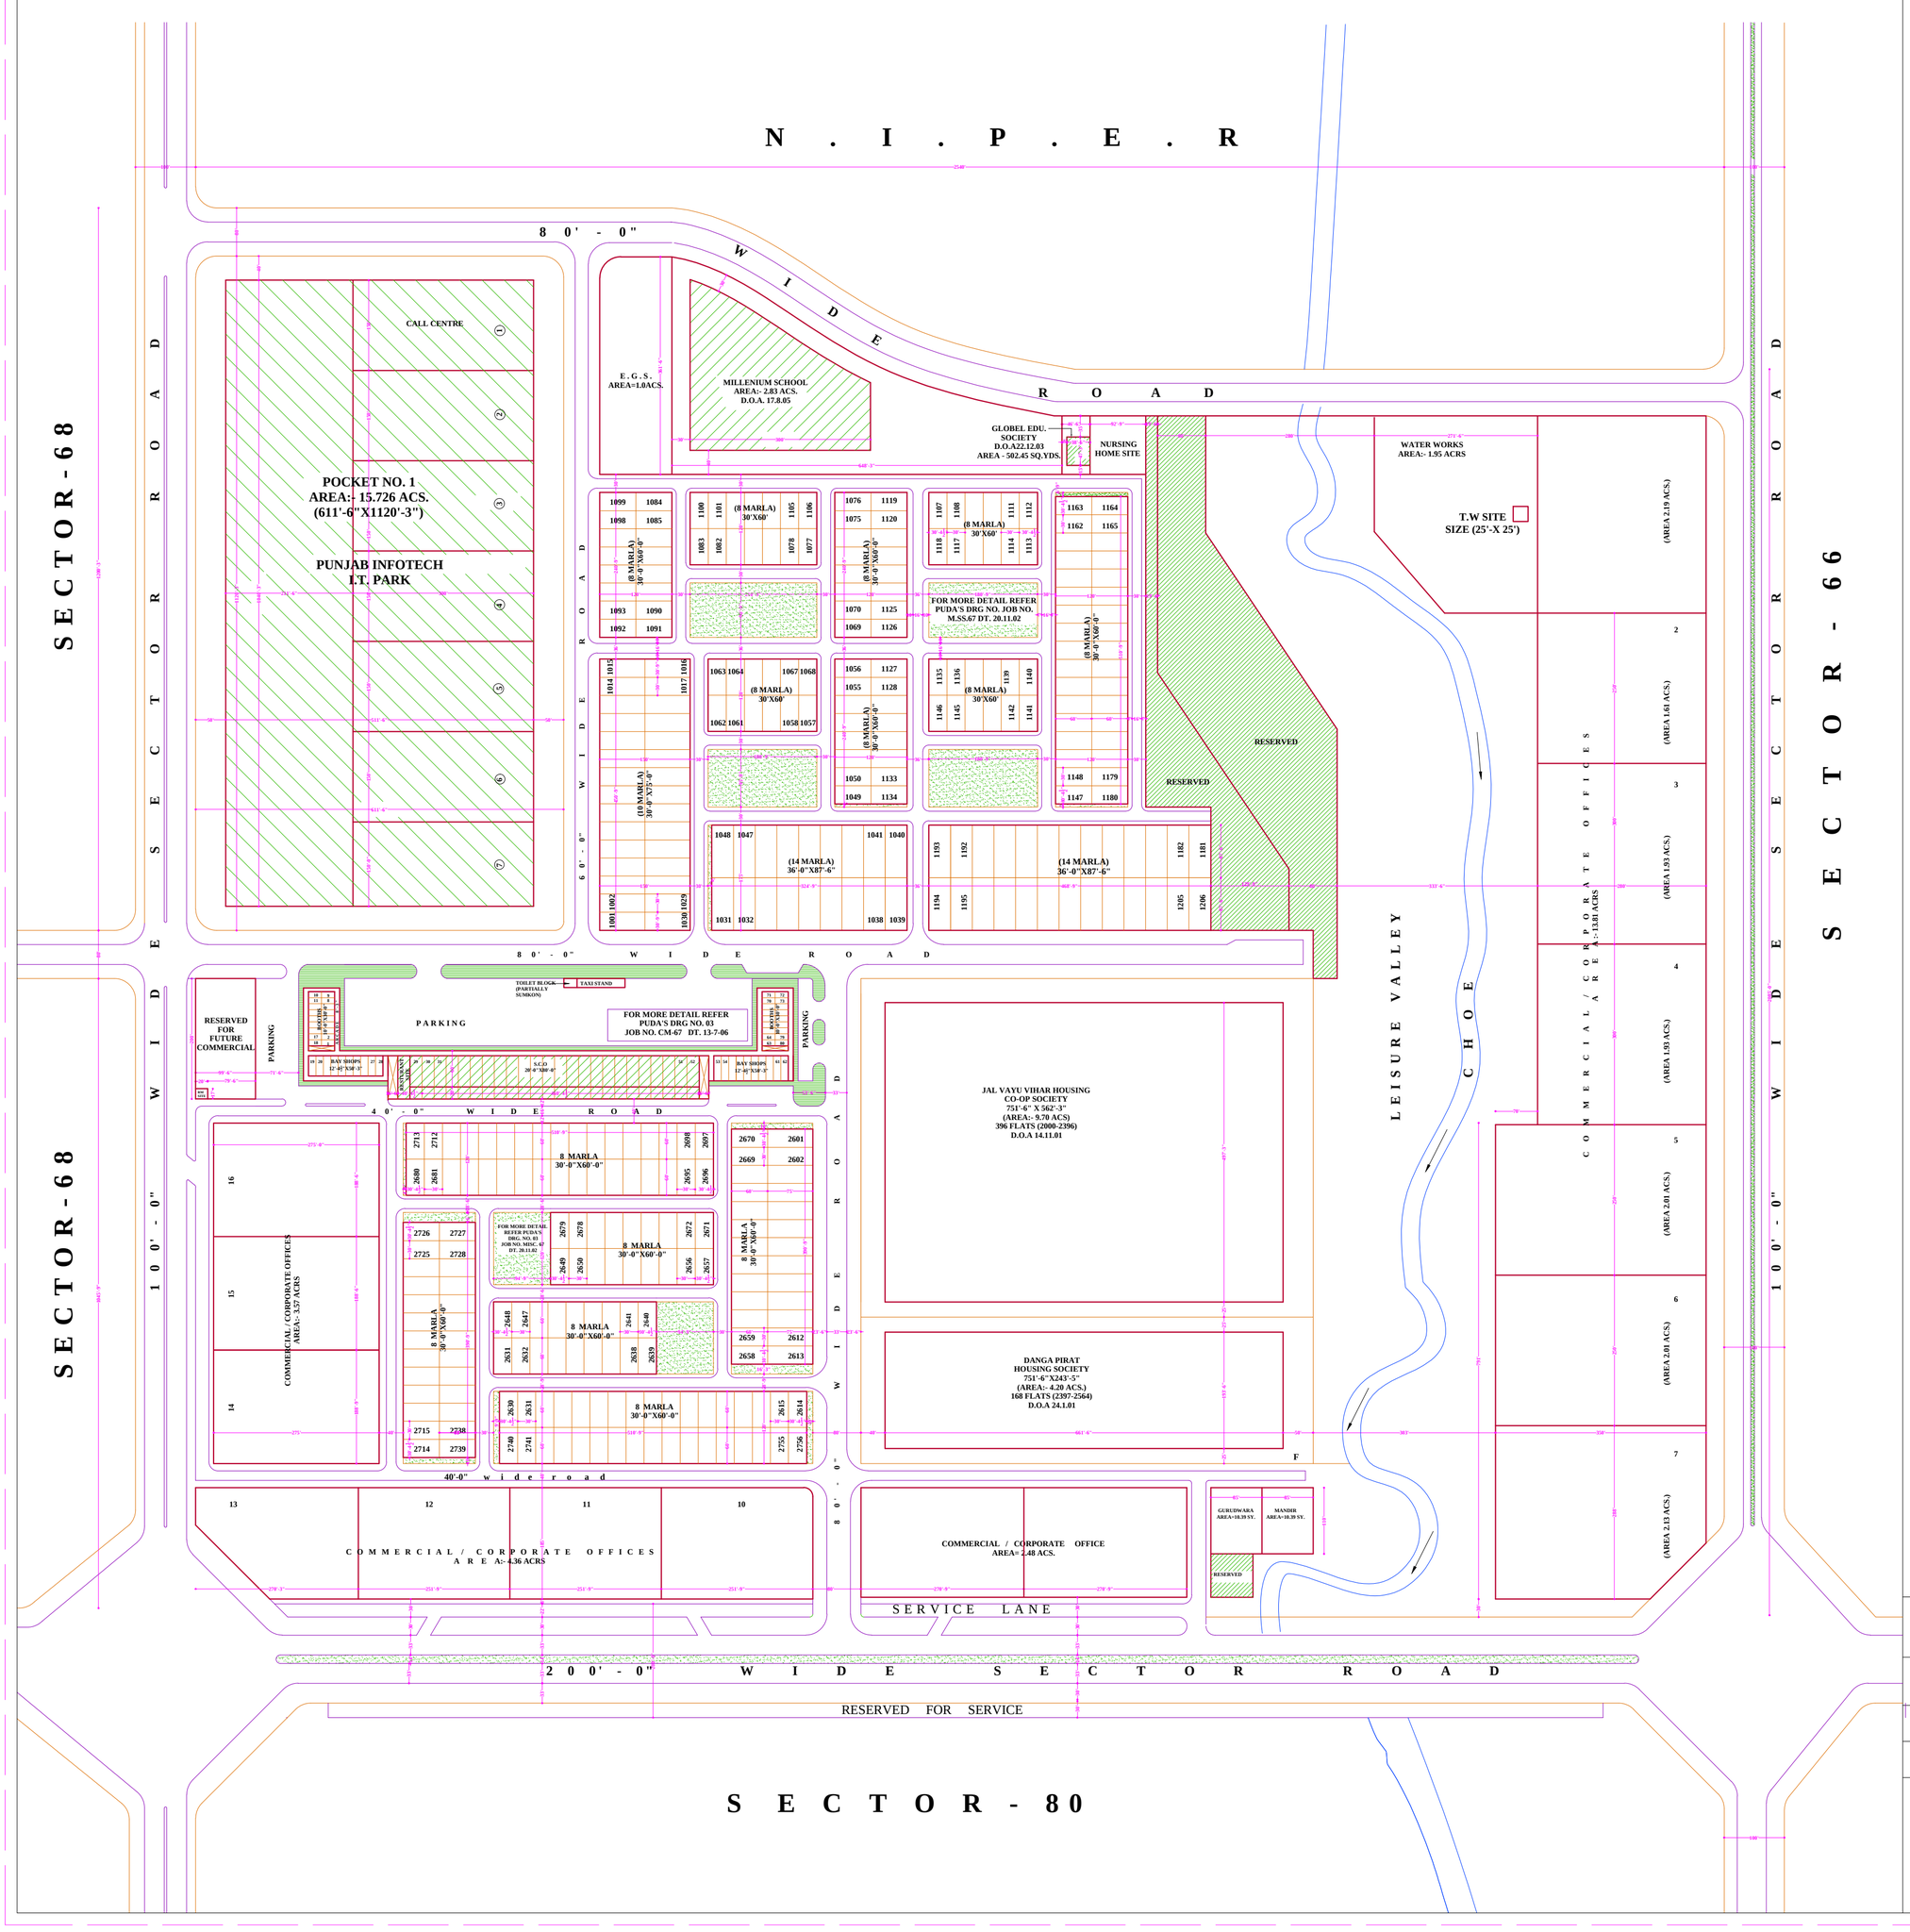

NOTE:-

THIS DIGITIZED DRAWING IS BASED ON THE ORIGINAL DRAWING OF THE CONCERNED DEPARTMENT. IN CASE OF ANY DISCREPANCY THE DETAILS IN THE ORIGINAL DRAWING SHALL PREVAIL UPON.

REVISED LAYOUT PLAN, SECTOR - 67

OFFICE OF THE DIVISIONAL TOWN PLANNER S.A.S NAGAR

DRG. NO: (D.T.P S.A.S. nagar)1410 / 2000 DATED: 14.2.2000

TRACED BY: CHECKED BY:

- Sd -	- Sd -	- Sd -	- Sd -
Assistant Planner	District Town Planner	Senior Town Planner	Chief Town Planner

REALTY HOLDING & MANAGEMENT CONSULTANTS
For any Mohali Real Estate question,
whatsapp us @91-7814613916
realtyconsultants.in