HOLDING & MANAGEMENT CONSULTANTS
REALTY
For any Mohali Real Estate question, whatsapp us @91-7814613916
realtyconsultants.in

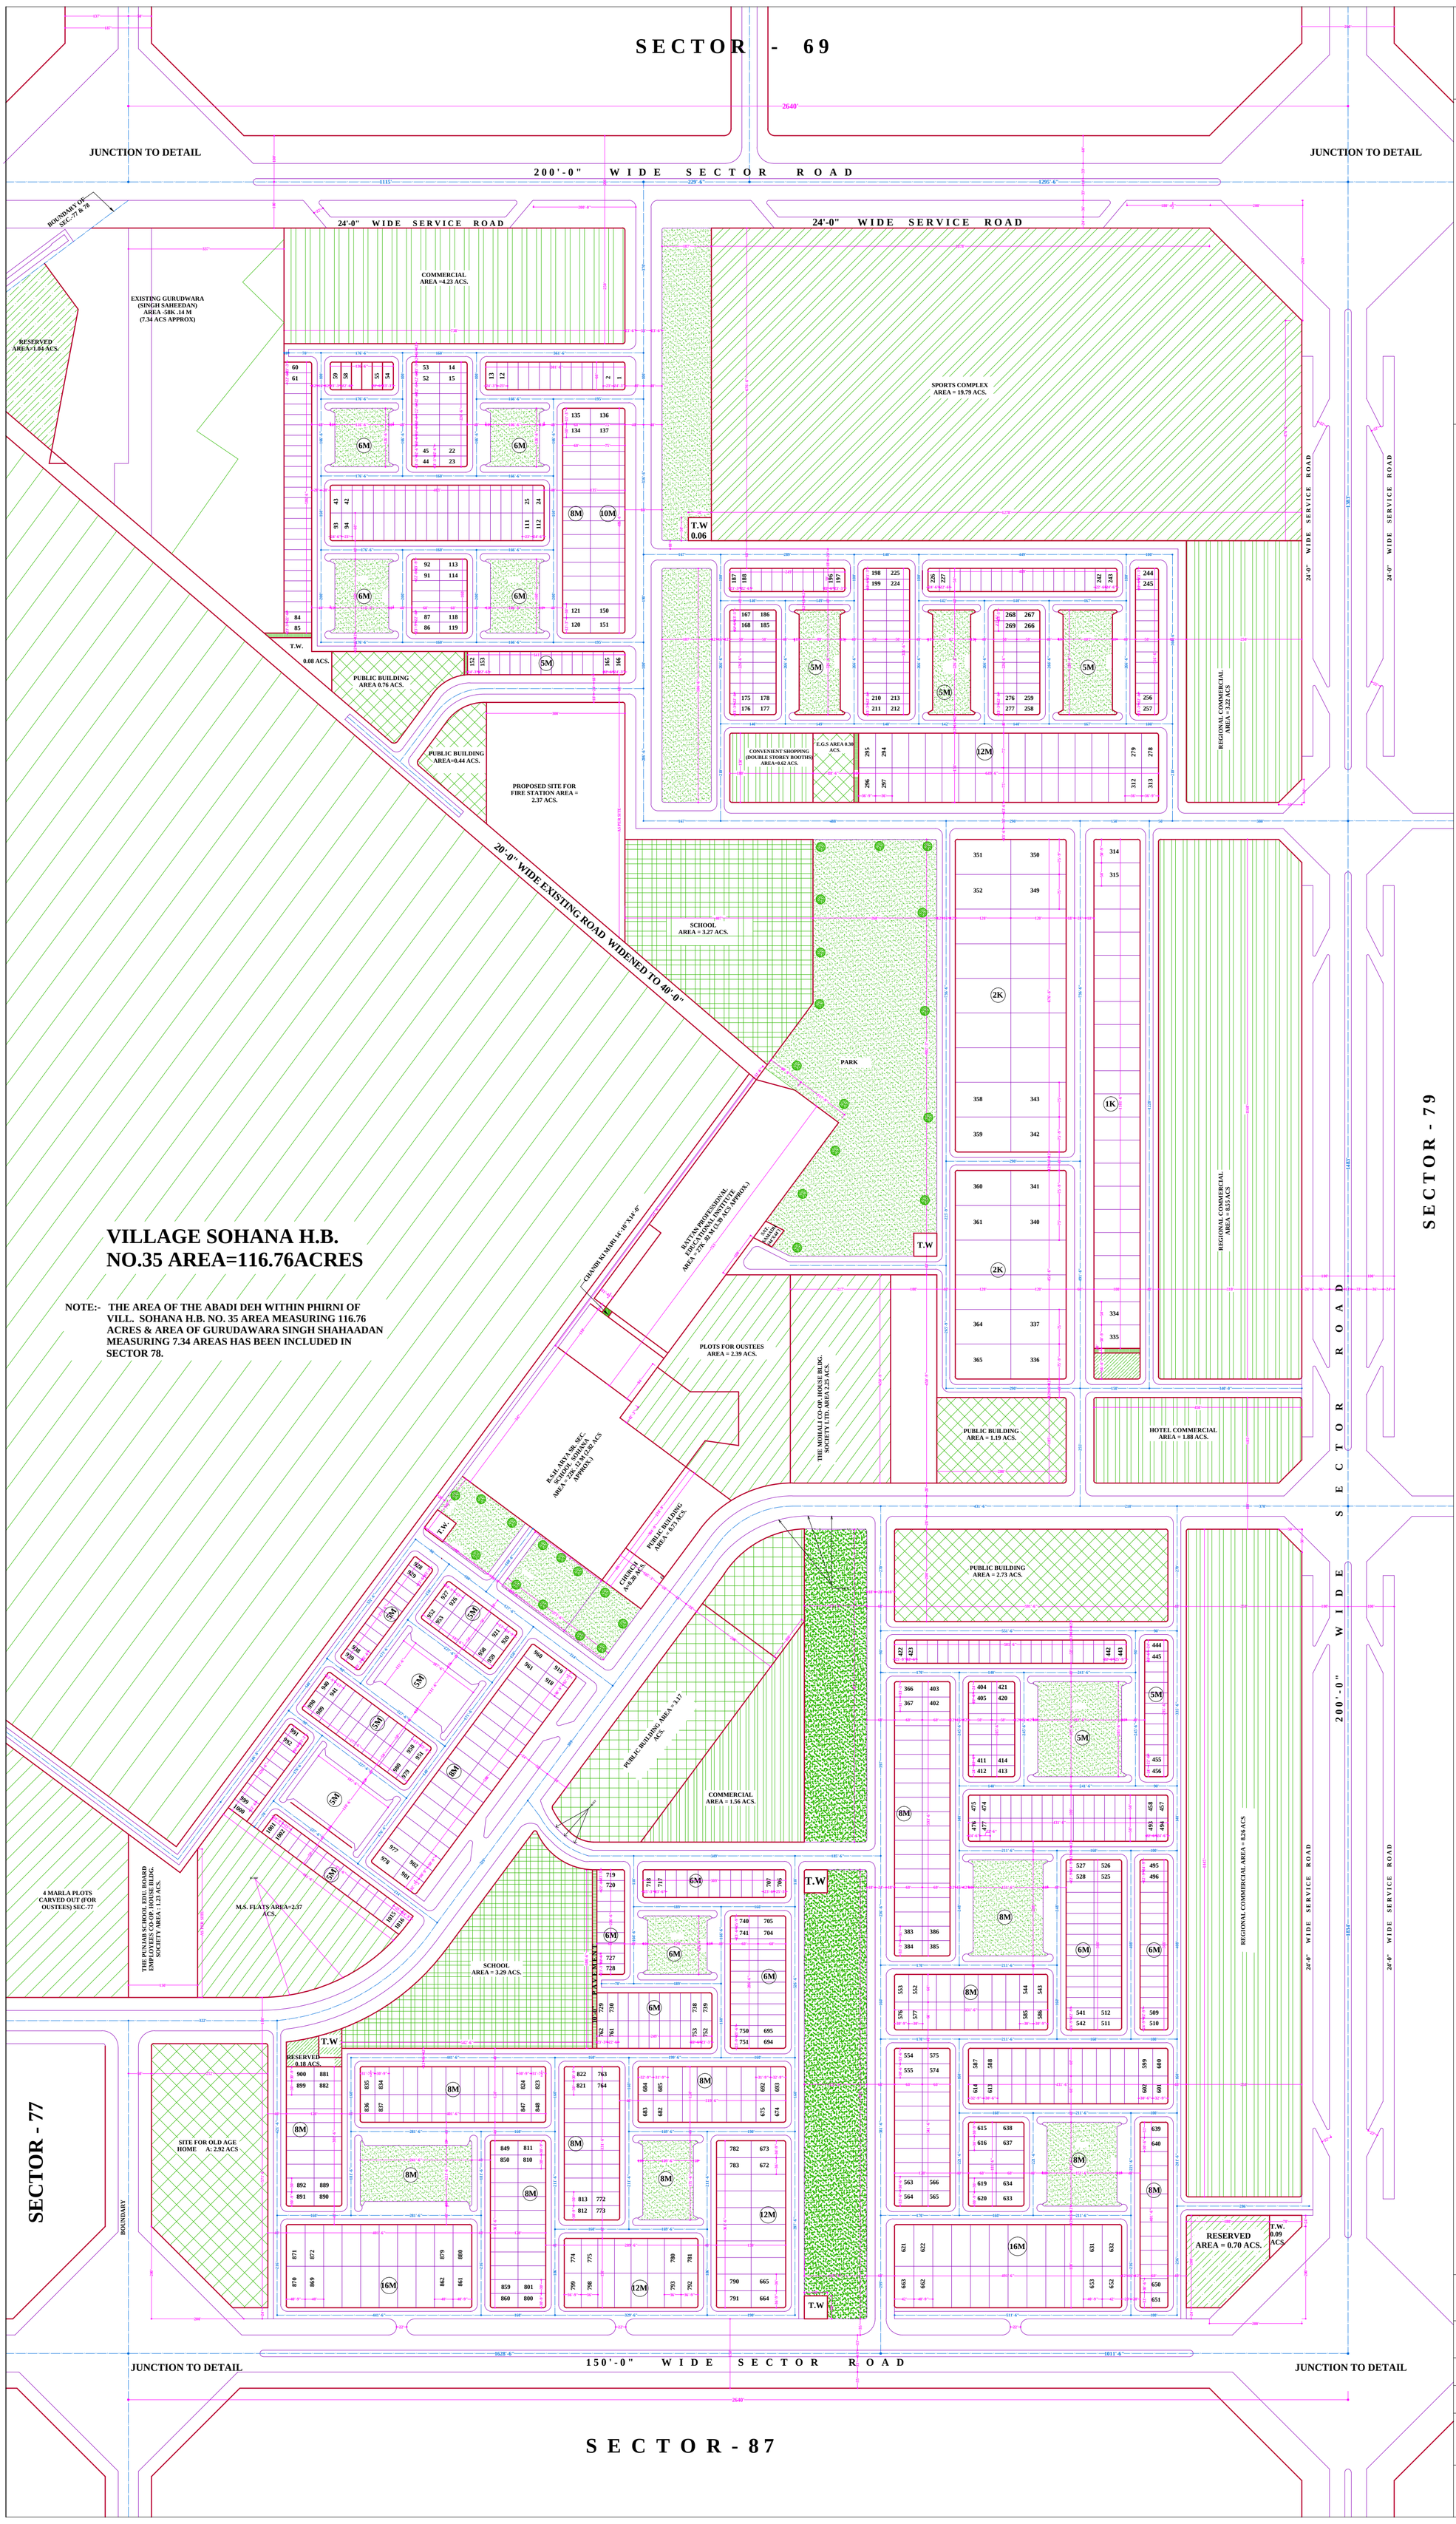

S.A.S. NAGAR
SECTOR - 78

SCALE: 1" = 100'-0"

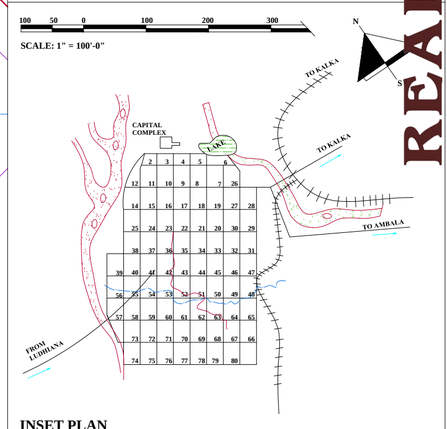

INSET PLAN

LEGEND:-

- Residential
- Multistoried flats
- Existing village sohana
- Commercial
- Educational
- Medical
- Public buildings
- Reserved
- Roads & open spaces
- Bus terminus
- T.W. — Tube well
- Pavement

DETAIL OF AREAS:-

	AREA IN ACS.		%AGE
Gross area of sector 78 (including vill. Sohana & gurudawara singh shaheedan)	356.99		
Area under peripherial roads	23.20		
Area of institution exempted			
Gurudawara Singh Shaheedan	7.34		
Rattan Professional Edu. Society	3.39	153.51	
B.S.H Arya School	2.82		
Area under village abadi	116.76		
Net planned area	203.48		
Area under residential including m.s. flats	53.45		26.27%
Area under commercial	28.32		13.92%
Area under educational	6.56		3.22%
Area under public building	13.15		6.46%
Area under bus stand	19.39		9.53%
Area under vet. hospital	1.42		0.70%
Area under religious	0.04		0.02%
Area under reserved	2.04		1.00%
Area under t.w.	0.29		0.14%
Area under roads & open spaces	78.82		38.74%
	203.48		100 %

SCHEDULED OF PLOTS:-

DETAIL OF RADII OF ROADS JUNCTION:-

JUNCTION BETWEEN ROAD		RADIUS
200	150	As per junction detail
200	100	As per junction detail
200	80	As per junction detail
150	100	As per junction detail
150	80	As per junction detail
100	100	35'-0"
100	80	35'-0"
100	60	30'-0"
100	40	25'-0"
80	80	30'-0"
80	60	30'-0"
80	40	25'-0"
60	60	25'-0"
60	40	20'-0"
40	40	15'-0"
40	24	15'-0"

- All corner plots marked (p) shall have 5'-0" radius.
- Boundary walls of public building, educational, institutions, m.s.flats & reserved pocket abutting the road junction shall have 15'-0" radii.

NOTES:-

- All measurements are to be exact & should be checked at site.
- All dimensions are to be taken from the centre line of carriage way which are shown in dash & dots.
- Detail of commercial pockets shall be supplied later.
- The layout cum demarcation plan has been approved by chief town planner vide endst. no. 1668-c.t.p. (pb.) / s.c-114 dated 28.7.2004 and in p & d committee meeting held on dt. 5.8.04.
- Tube well sites 7 nos. has been incorporated as per plans supplied by divisional engineer (ph-i) vide his letter no. d.e.(ph-i)/07/3609 dated 12.6.07. t.w. site area 0.09 acs. near junction sector 78-79 near reserved area has been merged in reserved pocket total area 0.70 +0.09 = 0.79 acs. as per detailed in rpd meeting dated:-
- Site for the mohali co-op house bldg. society ltd. allotted as per gmada's letter no. (gmada) / 2011/5861 dt. 25.04.2011.
- Site for the punjab school education board employees co-op house bldg. society allotted as per gmada's letter gmada (policy) /2011/5865 dt. 25.04.2011.
- Site for fire brigade station has been allotted as per gmada's letter no. gmada (policy) /2011/5980 dt. 27.04.2011 in lieu of vetrinary hospital.
- Site for church has been allotted vide gmada endst. no. gmada /e.o./2012/ 4109 dated 13.2.2012
- Planning of 4 marla size plots for oustees of sector-76 to 80 (near B.S.H. Arya School) has been approved by cheif town planner punjab vide memo no. 629 sc-114 vol.-3 dt. 31-01-2013

NOTE:-
THIS DIGITIZED DRAWING IS BASED ON THE ORIGINAL DRAWING OF THE CONCERNED DEPARTMENT. IN CASE OF ANY DISCREPANCY THE DETAILS IN THE ORIGINAL DRAWING SHALL PREVAIL UPON.

LAYOUT CUM DEMARCATION PLAN

OFFICE OF THE DIVISIONAL TOWN PLANNER S.A.S NAGAR

DRG. NO:D.T.P (S.A.S. nagar) /1688/2003 DATED: 14.7.2003

TRACED BY: - Sd - CHECKED BY: - Sd -

- Sd - Planning Officer			
- Sd - Asstt. Town Planner	- Sd - dist..Town Planner	- Sd - Senior Town Planner	- Sd - Chief Town Planner